Rev	Revision note	Created by	Checked by	Approved by	Date
0	RELEASE	ctbordupi	punfushafu	ctlwaterma	2025-10-10
1	Revised - overflow & door change pos	ctbordupi	punfushafu	ctlrelanra	2025-11-13

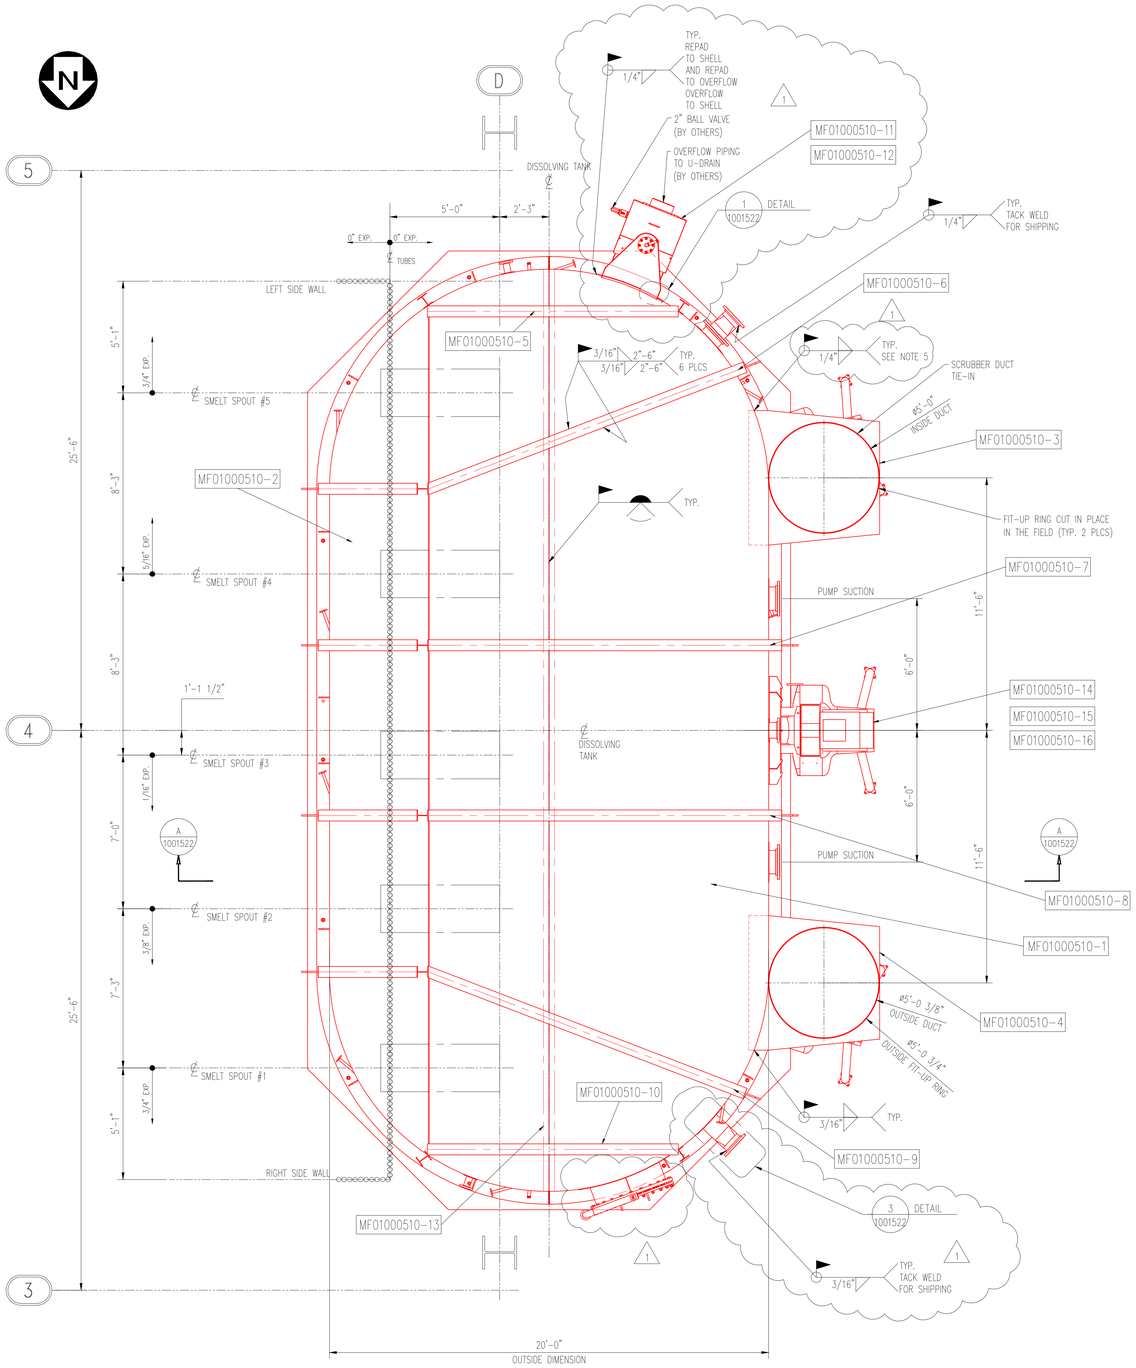

PLAN

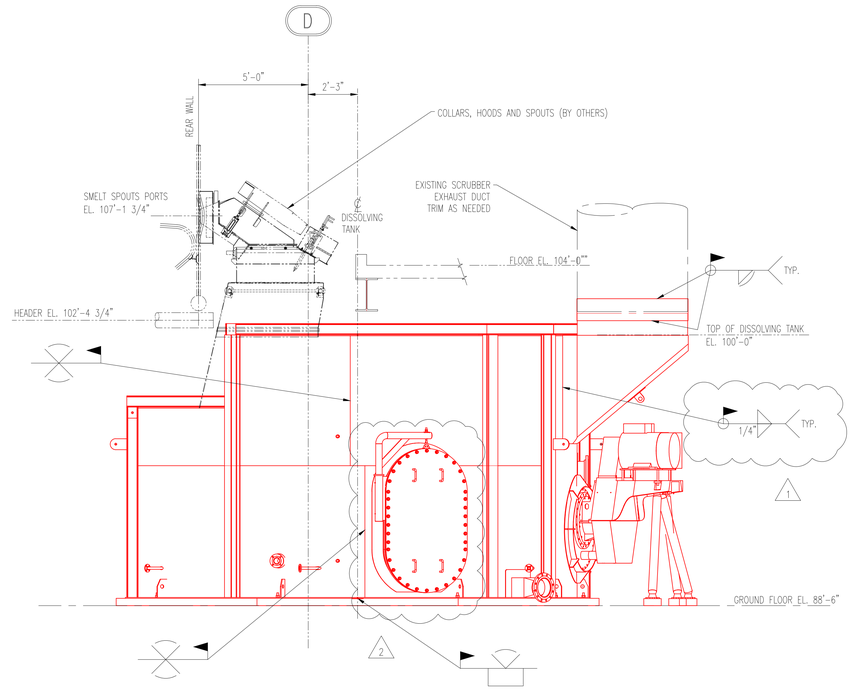

PARTIAL ELEVATION

(LOOKING SOUTH)

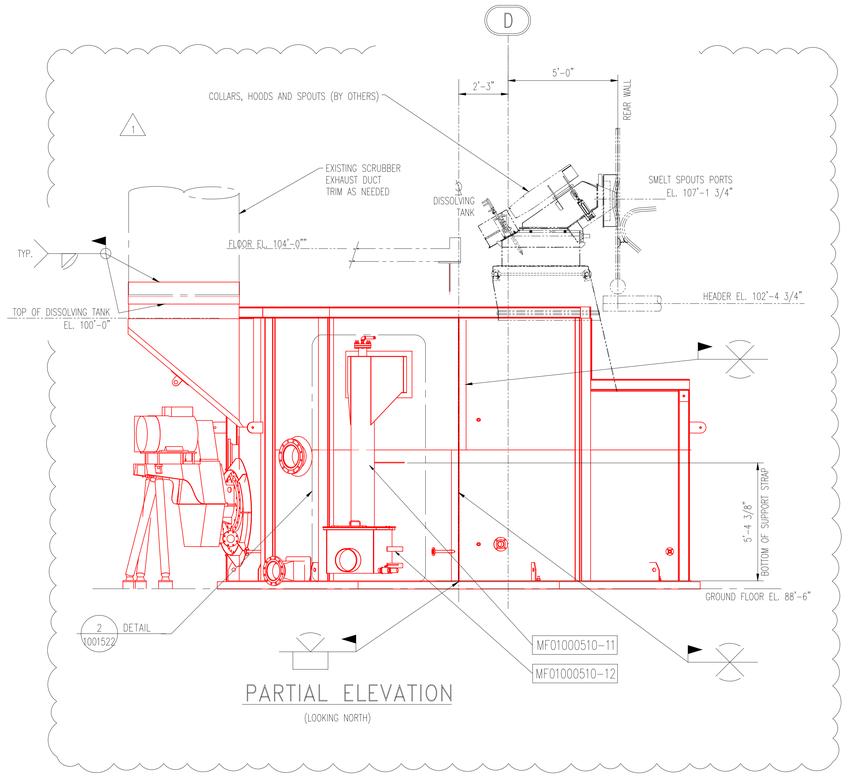

PARTIAL ELEVATION

(LOOKING NORTH)

SHIPPING UNIT INFORMATION

ASS'Y NO.	QTY.	DESCRIPTION	DRAWING NO.	WEIGHT PER ASS'Y
	1	POWP125274 CONSIT OF:		115426 LBS/EA
MF01000510-1	1	REAR HALF DISSOLVING TANK	MF00911582	52948 LBS/EA
MF01000510-2	1	FRONT HALF DISSOLVING TANK	MF00911582	54004 LBS/EA
MF01000510-3	1	SCRUBBER DUCT EXHAUST 1	MF00911582	1856 LBS/EA
MF01000510-4	1	SCRUBBER DUCT EXHAUST 2	MF00911582	1856 LBS/EA
MF01000510-5	1	STIFFENER BEAM 1	MF00911582	460 LBS/EA
MF01000510-6	1	STIFFENER BEAM 2	MF00911582	620 LBS/EA
MF01000510-7	1	STIFFENER BEAM 3	MF00911582	644 LBS/EA
MF01000510-8	1	STIFFENER BEAM 4	MF00911582	644 LBS/EA
MF01000510-9	1	STIFFENER BEAM 5	MF00911582	620 LBS/EA
MF01000510-10	1	STIFFENER BEAM 6	MF00911582	460 LBS/EA
MF01000510-11	1	OVERFLOW PIPE ASSEMBLY	MF00911582	670 LBS/EA
MF01000510-12	1	OVERFLOW TROUGH ASSEMBLY	MF00911582	400 LBS/EA
MF01000510-13	4	1/8" X 6" X 12' LG BACKING STRIP	MF01000510	244 LBS/EA
		POWP125277 CONSIST OF:		
MF01000510-14	1	AGITATOR (MOTOR AND FRAME)	MF01005171	3530 LBS/EA
MF01000510-15	1	AGITATOR (MOTOR AND FRAME)	MF01005171	3530 LBS/EA
MF01000510-16	1	AGITATOR (MOTOR AND FRAME)	MF01005171	3530 LBS/EA
		POWP125275 CONSIST OF: (SPARE)		
MF01000510-17	1	AGITATOR (ONLY)	MF01005171	3530 LBS/EA

REFERENCE DRAWINGS:

MF00911582 – DISSOLVING TANK ARRANGEMENT DRAWING
MF01001522 – ERECTION ARRANGEMENT – SECTION AND DETAILS

NOTES:

1. ALL DIMENSIONS AND EXISTING MATERIAL TO BE FIELD VERIFIED BY CONTRACTOR BEFORE ANY DEMOLITION OR INSTALLATION. ALL DIMENSIONS SHOWN ARE FIELD MEASUREMENTS.
2. DIMENSIONS AND ELEVATIONS SHOWN ARE FOR A COLD BOILER. VERTICAL EXPANSION AT THE LOOR TUBES IS APPROX. 9" DOWN. HORIZONTAL EXPANSION IS 0" AT REAR WALL OUTWARD.
3. COLLAR, HOODS AND SPOUT BY OTHERS. OPENING FOR COLLAR TO BE CUT ON SITE WITH SMELT SPOUT IN POSITION
4. SCRUBBER DUCTING TIE-IN TO BE FIT-UP AND OPENING IN DISSOLVING TANK CUT ON SITE.
5. ERECTOR TO TRIM EXCESS STACK DUCT INSIDE THE DISSOLVING TANK AS NEEDED.

POWP00xxxx – INDICATES VALMET PART NUMBER.
(x) – INDICATES VALMET ITEM NUMBER.

Project	P5115AUA1 GP Naheola RB4 - DT Repl
Mill	Naheola Mill
Equipment	Recovery Boiler
Device Position	
Item ID	POWP125274
Projection Method	
General Tolerances	ANSI B4.1
Welding Symbols	ANSI/AWS A2.4
Scale	3/8" = 1'-0"
Weight	lbs

This document is the exclusive intellectual property of Valmet Corporation and/or its subsidiaries subsidiaries (collectively and individually "Valmet") and is furnished solely for operating and maintaining the specific project. Re-use of the document for any other project or purpose is prohibited. The document or the information shall not be reproduced, copied or disclosed to a third party without prior written consent of Valmet. By accessing this document, you accept these terms of use.

Title: ERECTION ARRANGEMENT - DISSOLVING TANK PLAN VIEW

Issue Status: Certified for Construction		Document ID: MF01000510	Sheet: 1 of 1
Confidentiality: Internal	Document Type: Installation drawing		Revision: 1

Size: E AutoCAD